




DAVUM
PRECONTRAIT

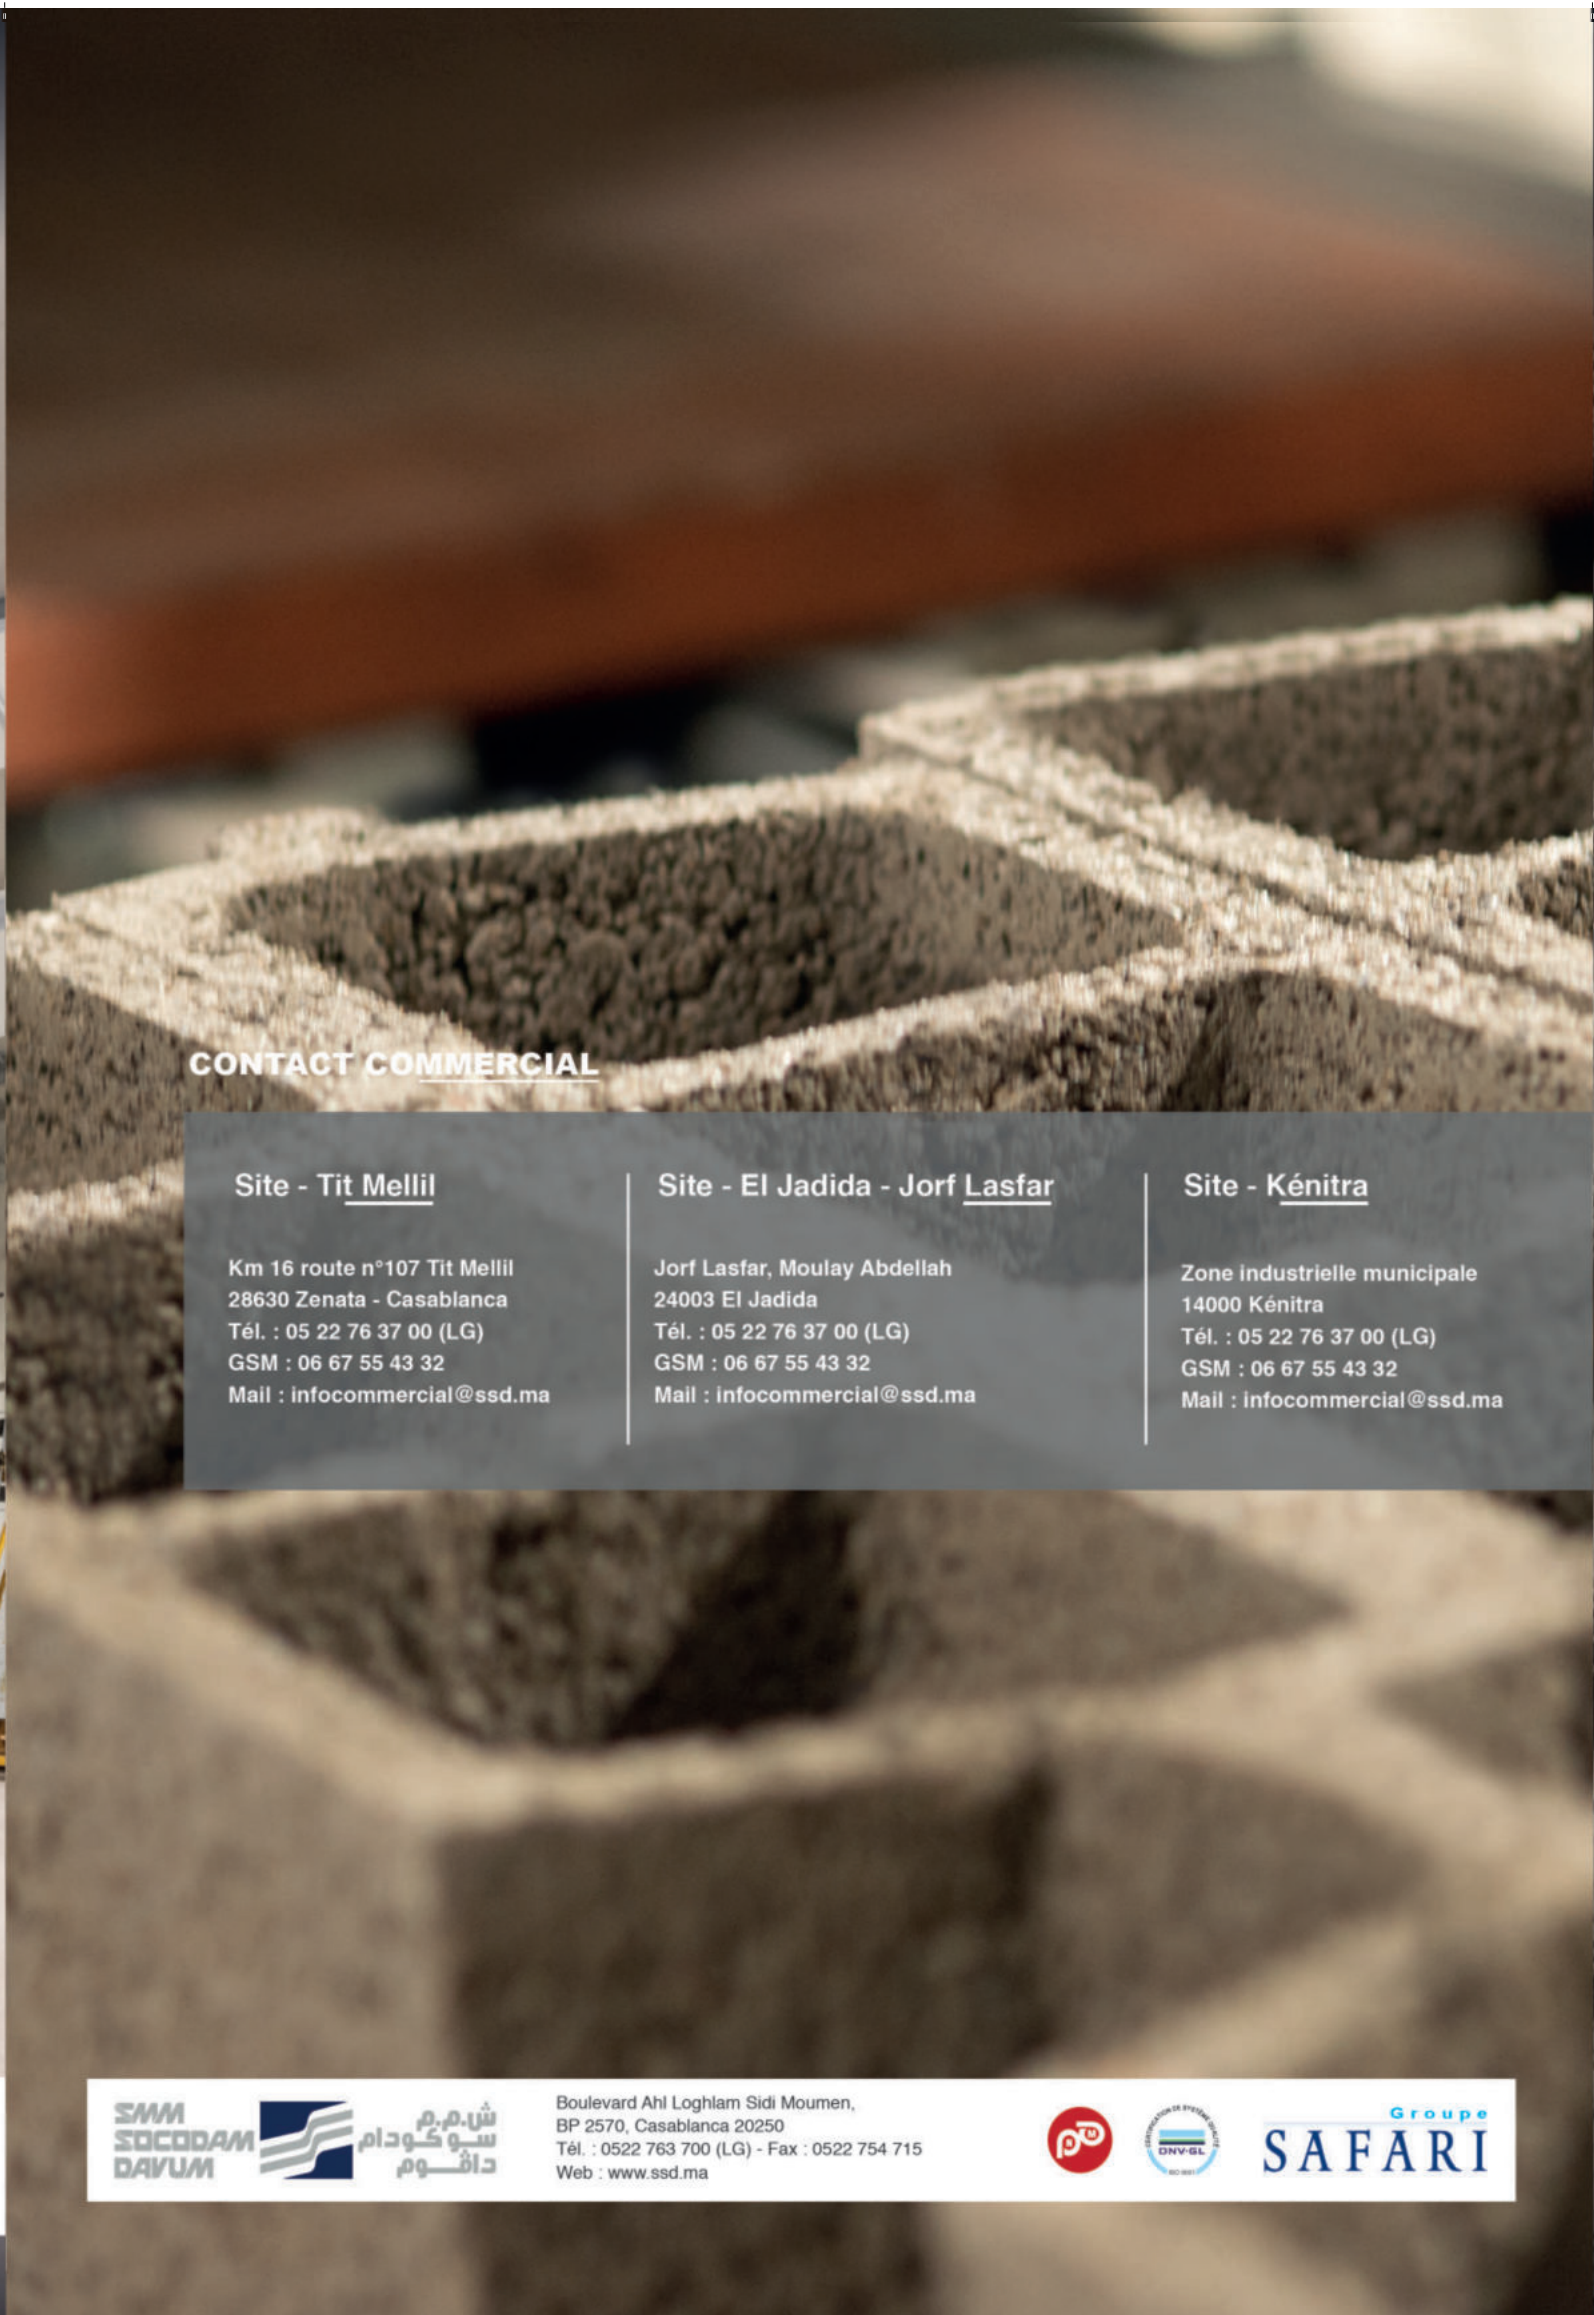

CONTACT COMMERCIAL

Site - Tit Mellil

Km 16 route n°107 Tit Mellil
28630 Zenata - Casablanca
Tél. : 05 22 76 37 00 (LG)
GSM : 06 67 55 43 32
Mail : infocommercial@ssd.ma

Site - El Jadida - Jorf Lasfar

Jorf Lasfar, Moulay Abdellah
24003 El Jadida
Tél. : 05 22 76 37 00 (LG)
GSM : 06 67 55 43 32
Mail : infocommercial@ssd.ma

Site - Kénitra

Zone Industrielle municipale
14000 Kénitra
Tél. : 05 22 76 37 00 (LG)
GSM : 06 67 55 43 32
Mail : infocommercial@ssd.ma

SMM
SOCODAM
DAVUM



ش.م.م
سوكودام
داڤوم

Boulevard Ahi Lghlam Sidi Moumen,
BP 2570, Casablanca 20250
Tél. : 0522 763 700 (LG) - Fax : 0522 754 715
Web : www.ssd.ma



Groupe
SAFARI



Plancher précontraint

- Poutrelles précontraintes
- Treillis soudés
- Hourdis
- Agglos

DAVUM
PRECONTRAIT

www.ssd.ma




Smm-Socodam-Davum

Plus d'un demi-siècle d'expertise dans le plancher préfabriqué

Première entreprise à avoir introduit le plancher préfabriqué au Maroc, **Smm-Socodam-Davum** s'impose, avec ses marques **DAVUM** et **DAVUM PRECONTRAIN**, comme une référence incontournable sur le marché au-delà des exigences des professionnels du secteur.

- Assistance technico-commerciale en permanence.
- Réalisation de plans de pose adaptés aux besoins des professionnels.
- Couverture nationale assurée via divers sites de production et agences commerciales.

Les planchers '**DAVUM PRECONTRAIN**' répondent aux règles du CPT (Cahier des Prescriptions Techniques).

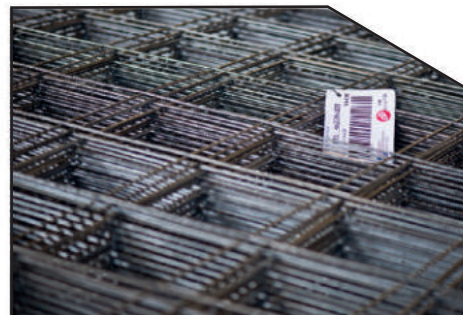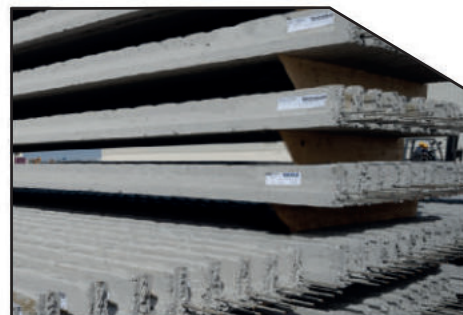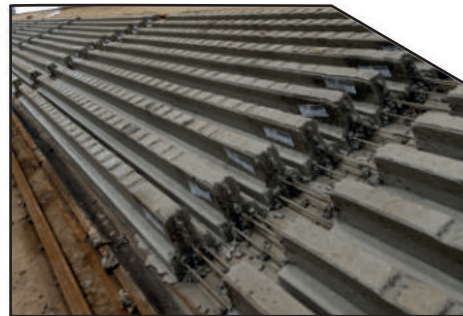

Poutrelles précontraintes

Les poutrelles **DAVUM PRECONTRAIN** sont des éléments porteurs, fabriquées avec des armatures adhérentes, plus résistantes et composées essentiellement de béton à hautes performances. Leur section est en forme de T renversé dont, l'âme s'évase légèrement vers le haut.

Les faces latérales de l'âme présentent une rugosité brute de filage. La partie supérieure de la poutrelle est traitée afin d'obtenir une rugosité marquée.

Les fils d'aciers Ø4 (1860* – TBR**) et Ø5 (1860 – TBR) constituent les armatures de précontrainte de base. Les poutrelles **DAVUM PRECONTRAIN** permettent d'atteindre de grandes portées de 4.97 m de long sans étais et de 9.59 m avec étais.

Elles offrent une grande liberté de conception des bâtiments, en réduisant sensiblement la nécessité des murs porteurs intérieurs.

Domaine d'utilisation

Domaine englobant les utilisations courantes telles que les planchers sur vides sanitaires, hauts de caves et sous-sols, étages courants, planchers terrasses, planchers de combles, utilisés en maisons individuelles, immeubles collectifs, groupes scolaires, bâtiments hospitaliers, bureaux, commerces, etc., situés en toutes zones géographiques, qu'elles soient sismiques ou non.

Treillis soudés


Smm-Socodam-Davum est la première entreprise à avoir certifié ses treillis soudés selon la norme marocaine **NM.01.4.220**.

- Une large gamme de treillis soudés constitués de fils d'aciers tréfilés de nuances FeE500 crantés ou lisses.
- Un stock permanent en différentes mailles et dimensions.

Gamme de produits

Les poutrelles **DAVUM PRECONTRAIN** existent en trois types dont, les principales caractéristiques géométriques sont indiquées dans le tableau suivant :


Type	Armature de précontrainte [mm]	Hauteur [mm]	Poids [daN/m]	Largeur talon [mm]
110	Ø 4 ou bien Ø 5 -1860-TBR	110	16.6	100
130	Ø 5-1860-TBR	130	20.1	100
150	Ø 5-1860-TBR	150	29.3	130

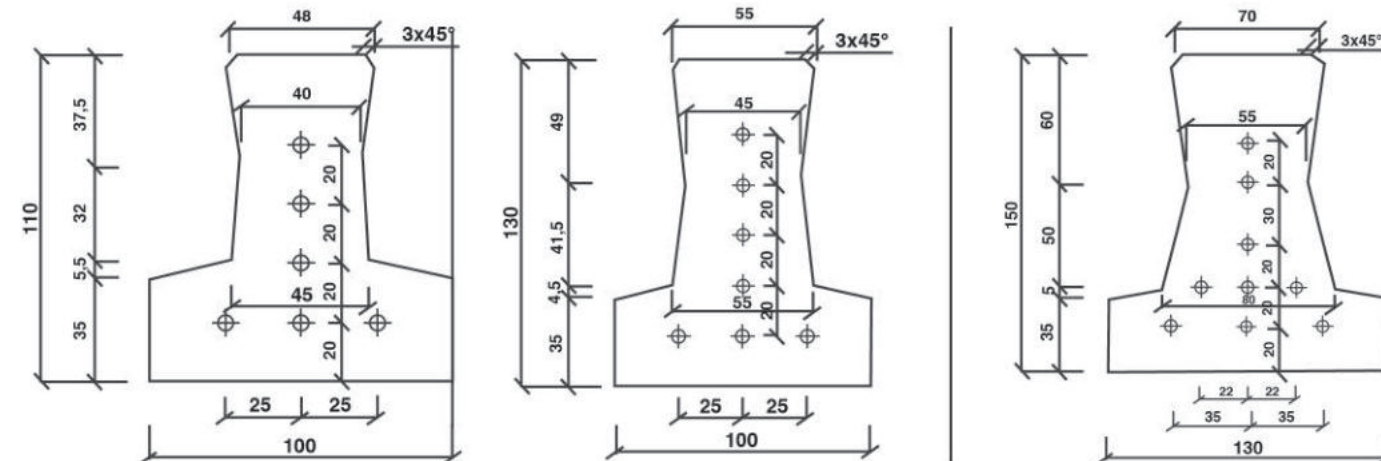

Stockage sur chantier

Pour un stockage sur chantier, il est essentiel de respecter certaines règles :

- Les poutrelles doivent être entreposées sur un terrain nivelé capable de supporter la charge sans enfoncement. L'utilisation de chevrons alignés entre les poutrelles facilite leur reprise.
- Les chevrons doivent être impérativement superposés pour éliminer les efforts parasites. Il est crucial de respecter correctement les porte-à-faux maximum.
- Une attention particulière doit également être portée à la hauteur d'empilement maximale du stock des poutrelles.
- Les poutrelles doivent être placées sur deux appuis aussi proches que possible de leurs extrémités, sans dépasser 50 cm.

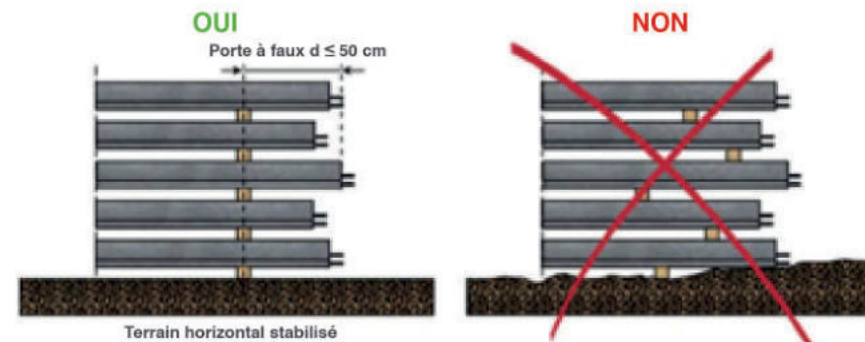

Poutrelle DAVUM en béton précontraint

Manutention

Afin de faciliter la manutention, les poutrelles **DAVUM PRECONTRAIN**, dont la longueur béton dépasse 2 mètres, peuvent être équipées de poignées à chaque extrémité. Ces poignées sont réalisées en acier lisse ou en matière plastique. Ce dispositif, conçu exclusivement pour une préhension manuelle, ne doit en aucun cas être utilisé comme point d'attache d'élingues de levage.

Traçabilité

Les poutrelles **DAVUM PRECONTRAIN** sont munies d'une étiquette indiquant leur dimension, le système de plancher comprenant par exemple le nom du site de production et le type de poutrelle. Ces éléments garantissent la traçabilité des produits jusqu'au moment de leur incorporation dans l'ouvrage.

Portées limites des planchers DAVUM PRECONTRAIN

CARACTERISTIQUES DU MONTAGE PPS136				EXP CHARGES DaN/M2 PPS136			
				CLOISONS = 75/REV.SOL =175/CH.EXPL=150			
MONTAGE	POIDS DU MONTAGE daN/ M2	LITRAGE L/m²	ENTRAXE cm				
12+4	239	47	60	3,96	4,19	4,59	5,51
16+4	282	58	60	3,95	5,01	5,55	6,60
20+5	348	79	60	3,67	5,85	6,41	7,73
25+5	433	95	63	4,41	6,99	7,72	9,29

Corps creux pour planchers (Hourdis)

Smm-Socodam-Davum offre une large gamme de corps creux concus pour le plancher **DAVUM PRECONTRAIN**, adaptée à tous types de bâtiments : H8 - H12 - H16 - H20 - H25


Les entrevous de type **DAVUM PRECONTRAIN** sont utilisés comme un coffrage pour le plancher précontraint. Ils sont conformes aux normes en vigueur, offrent une bonne résistance au feu, et contribuent à améliorer les performances d'isolation thermique et acoustique du plancher.

Blocs en béton pour murs et cloisons (Agglos)

Certifiés selon la norme **NM.10.1.009**, les agglos **DAVUM PRECONTRAIN** sont réputés par les professionnels du bâtiment, pour leur résistance et leur uniformité.

- Facilité de mise en œuvre sur les chantiers.
- Un isolant acoustique performant.
- Résistance au feu :
 - Paroi en agglos creux 150 mm classée CF 120 min.
 - Paroi en agglos creux 200 mm classée CF 150 min.
- Choix de différentes dimensions :
 - Agglos 7, Agglos 10, Agglos 15, Agglos 20.

Eléments constitutifs d'un plancher à poutrelles précontraintes

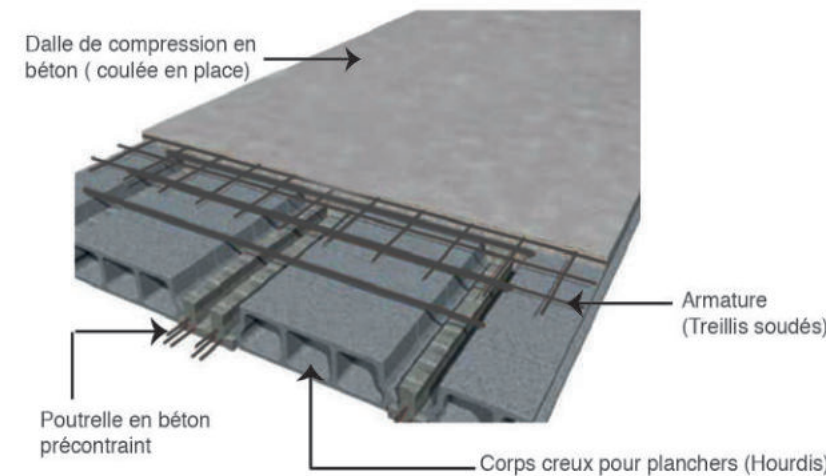

DAVUM
PRECONTRAIN

(*) Classe normative 1860
(**) TBR : très basse relaxation